

Dist

COUNTY

ROUTE

POST MILES
TOTAL PROJECT

SHEET
No.

TOTAL
SHEETS

REGISTERED CIVIL ENGINEER


X
DATE

PLANS APPROVAL DATE

X
No. X
Exp. X
CIVIL
STATE OF CALIFORNIA

THE STATE OF CALIFORNIA OR ITS OFFICERS OR AGENTS
SHALL NOT BE RESPONSIBLE FOR THE ACCURACY OR
COMPLETENESS OF SCANNED COPIES OF THIS PLAN SHEET.

THE REGISTERED CIVIL ENGINEER FOR THE PROJECT IS RESPONSIBLE FOR THE SELECTION
AND PROPER APPLICATION OF THE COMPONENT DESIGN AND ANY MODIFICATIONS SHOWN.

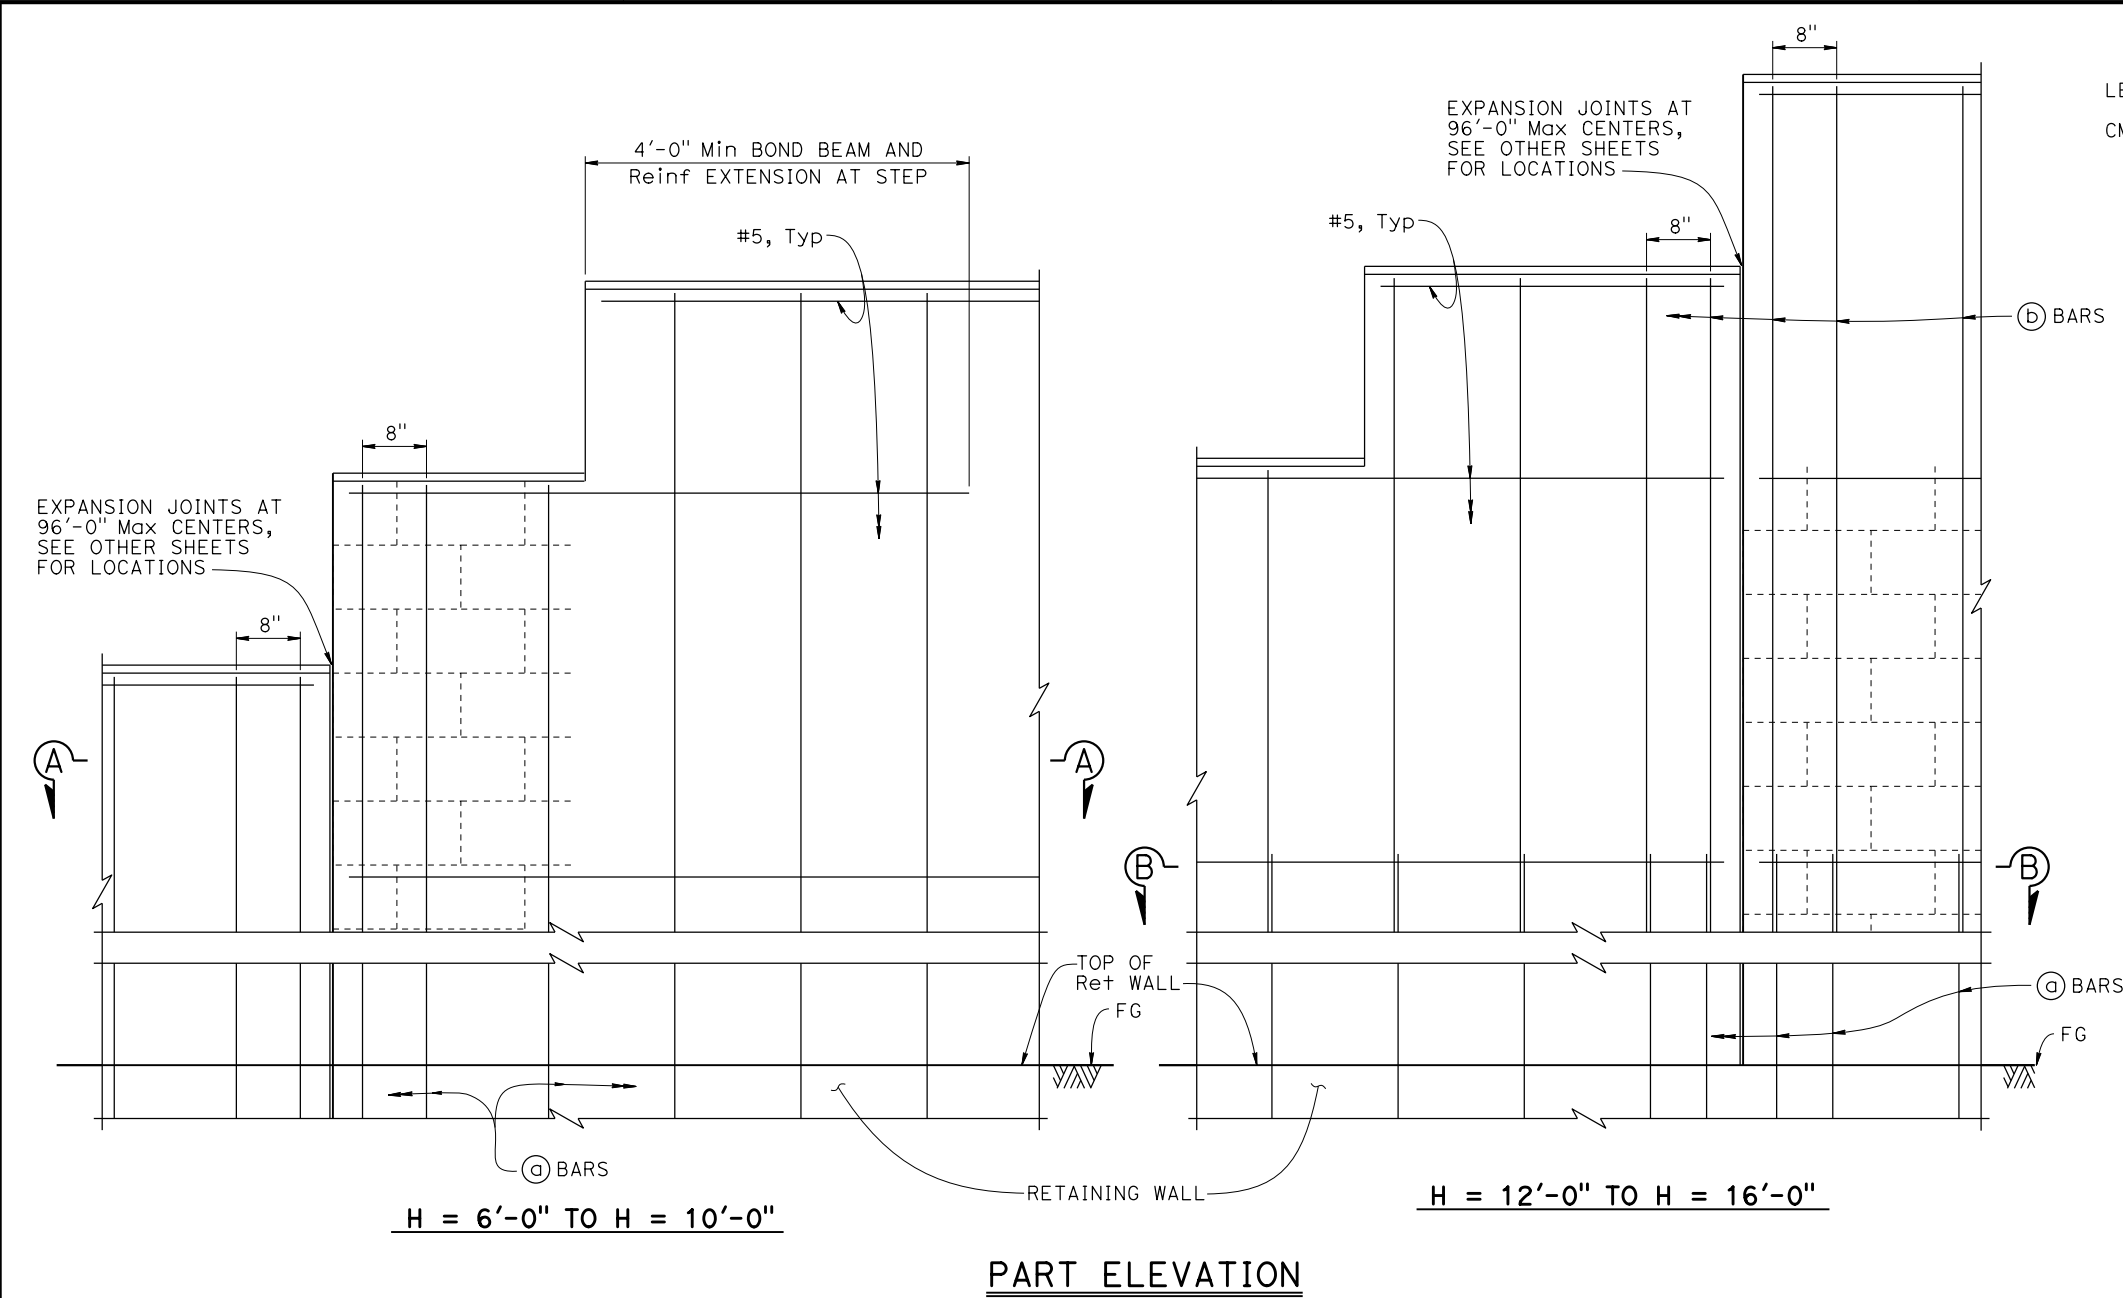

LEGEND:
CMU - Concrete Masonry Unit

SOUND WALL REINFORCEMENT TABLE			
MAXIMUM H	(a) BARS @ 16 Max	(b) BARS @ 16 Max	"Y" **
6'-0"	#4	---	---
8'-0"	#4	---	---
10'-0"	#4	---	---
12'-0"	#5	#4	6'-0"
14'-0"	#6	#4	8'-0"
16'-0"	#6	#4	10'-0"

** For "Y", see "SW MASONRY BLOCK ON RW DETAILS No. 2" sheet.

GENERAL NOTES
LOAD AND RESISTANCE FACTOR DESIGN

DESIGN:
AASHTO LRFD Bridge Design Specifications,
2017 edition with California Amendments
TMS 402-16, 2019 California Building Code

SEISMIC LOADING:
0.57 x Dead load


WIND LOADING:
0.0365 ksf

REINFORCED CONCRETE:
 $f_y = 60 \text{ ksi}$
 $f'_c = 3.6 \text{ ksi}$
 $f'_m = 2 \text{ ksi}$ for normal CMU block *
 $f'_m = 2.5 \text{ ksi}$ for high-strength CMU block *

* Provide materials to achieve the net compressive strength of concrete masonry unit equal to or greater than specified f'_m .

- NOTES:
- For type of block and joint finish, see other sheets.
 - When blocks are laid in stacked bond, ladder type, galvanized joint reinforcement shall be provided. Galvanized joint reinforcement must be a minimum of two continuous W9 wires at 4'-0" maximum spacing. Locate reinforcement in joints that are at the approximate midpoint between bond beams.
 - Horizontal joints shall be tooled concave or may be weathered. Vertical joints shall be tooled concave or may be raked.
 - For intermediate sound wall heights that are between the heights given, use the tabular information for the next higher "H".
 - For sound wall details not shown, see Standard Plan B15-9.

NO SCALE

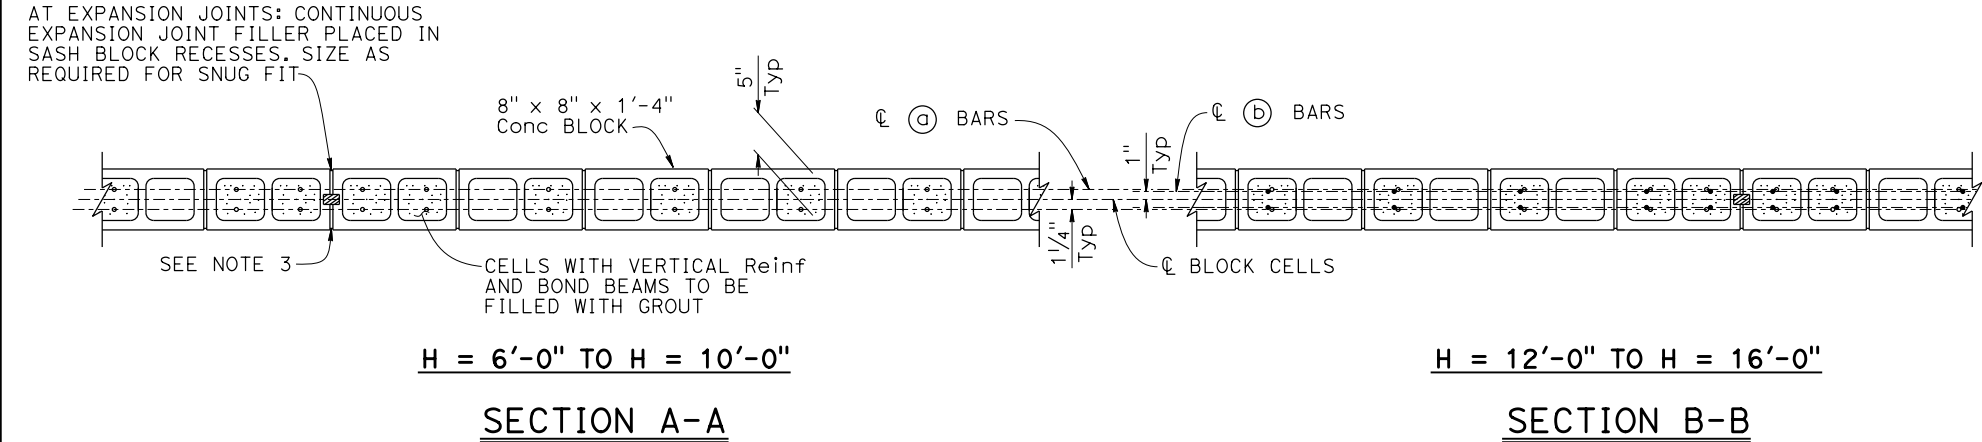

NOTE: For details not shown, see "SECTION A-A".