

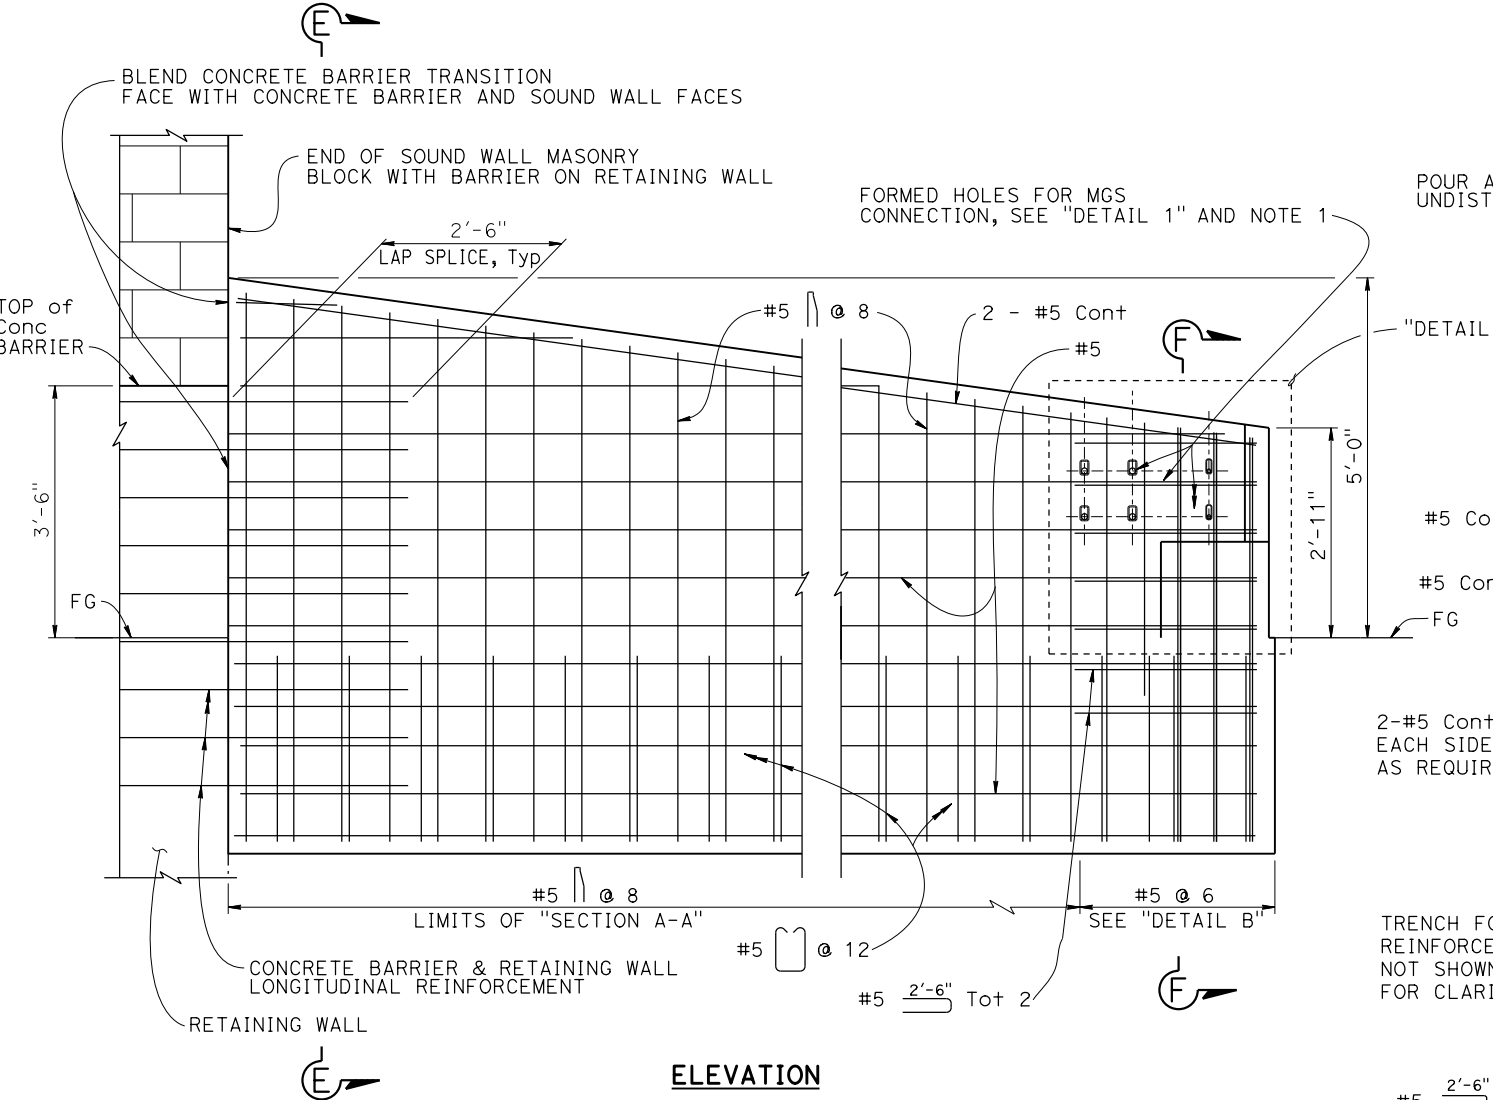



- NOTES:
- Adjust reinforcement as needed to provide 1" minimum clearance to HSS section.
 - Concrete barrier transition at departure is similar to concrete barrier transition at approach except as shown on "SOUND WALL MASONRY BLOCK WITH BARRIER ON RETAINING WALL DETAILS No. 2" sheet.

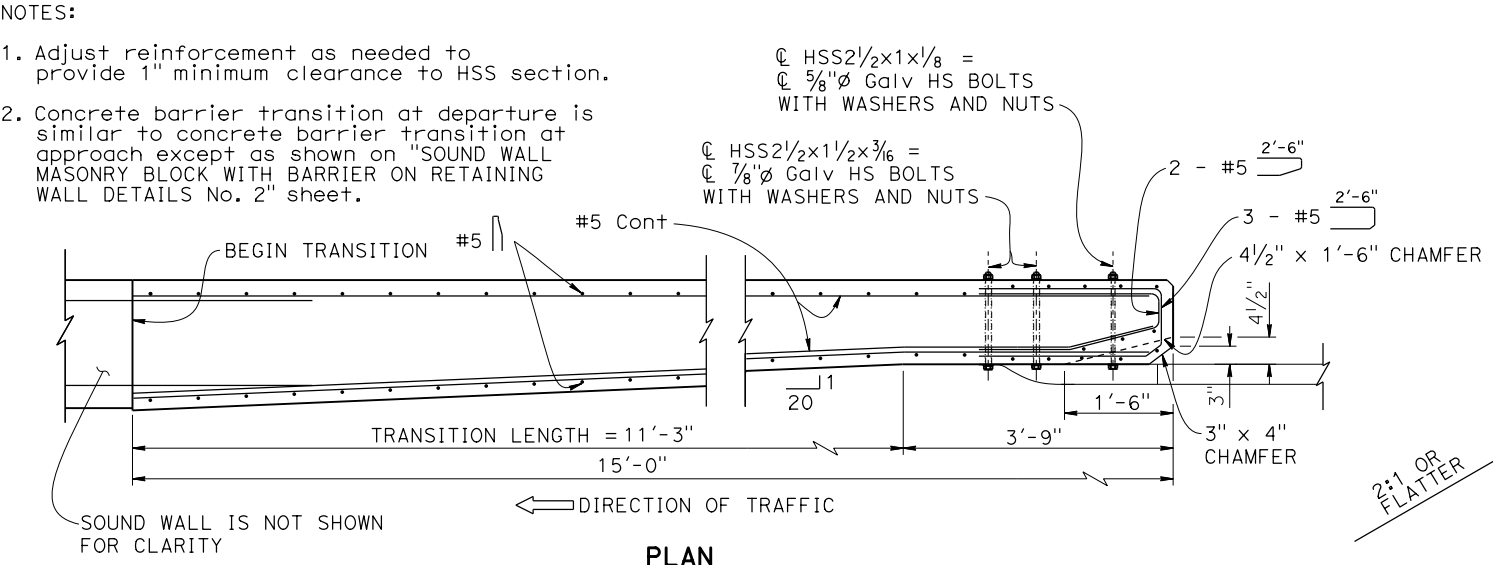


CONCRETE BARRIER TRANSITION AT APPROACH
See Note 2

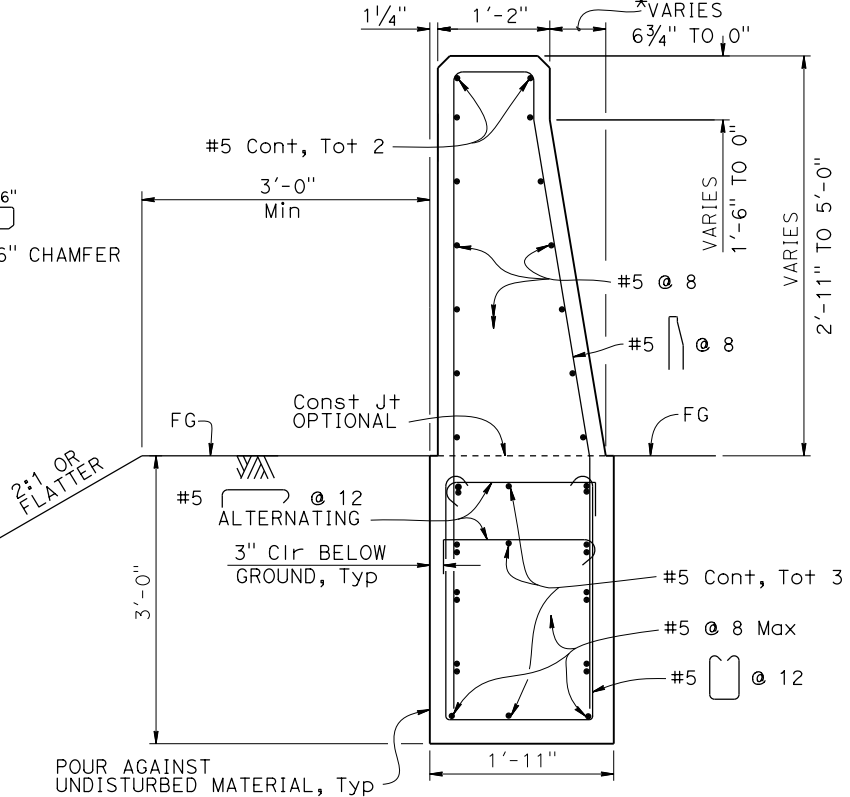


SECTION E-E

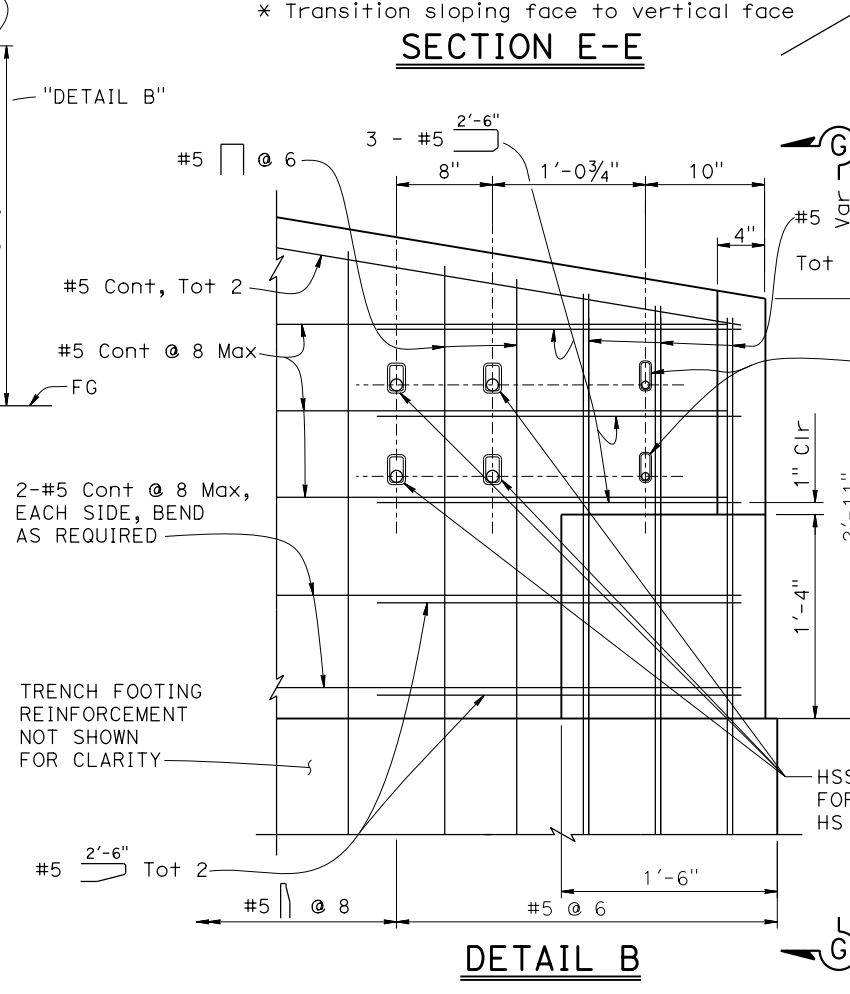

DETAIL B

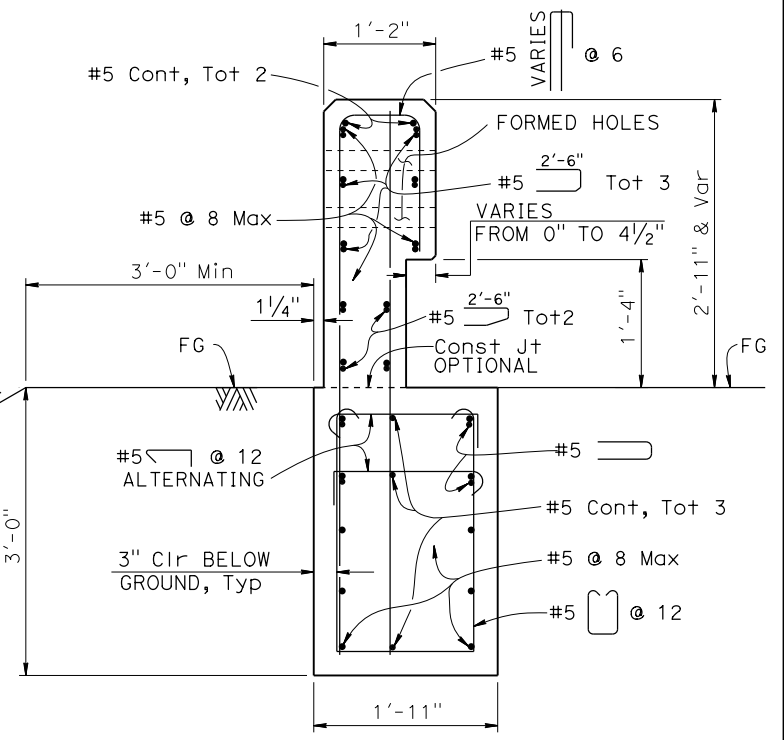

SECTION F-F

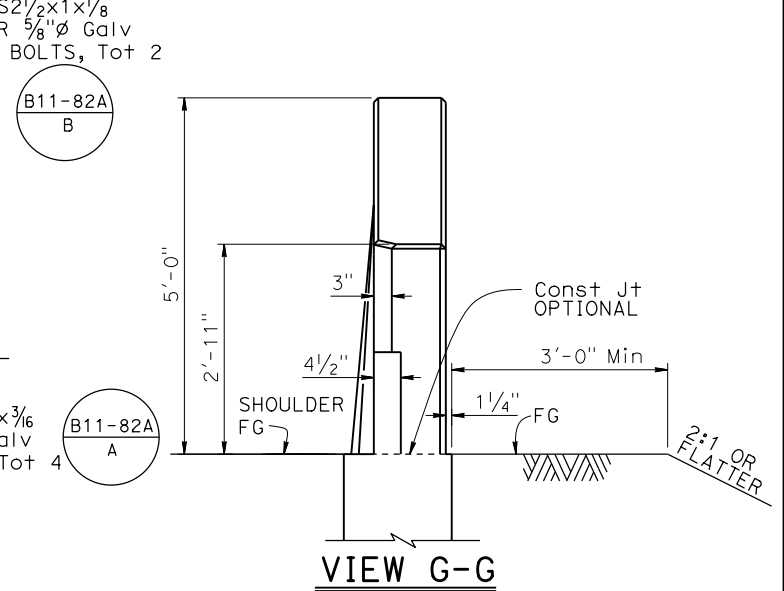

VIEW G-G

NO SCALE

DIST	COUNTY	ROUTE	POST MILES TOTAL PROJECT	SHEET NO.	TOTAL SHEETS

REGISTERED CIVIL ENGINEER X DATE

PLANS APPROVAL DATE

THE STATE OF CALIFORNIA OR ITS OFFICERS OR AGENTS SHALL NOT BE RESPONSIBLE FOR THE ACCURACY OR COMPLETENESS OF SCANNED COPIES OF THIS PLAN SHEET.

THE REGISTERED CIVIL ENGINEER FOR THE PROJECT IS RESPONSIBLE FOR THE SELECTION AND PROPER APPLICATION OF THE COMPONENT DESIGN AND ANY MODIFICATIONS SHOWN.