

Dist

COUNTY

ROUTE

POST MILES
TOTAL PROJECT

SHEET
NO.

TOTAL
SHEETS

REGISTERED CIVIL ENGINEER

X
DATE

PLANS APPROVAL DATE


X
No. X
Exp. X
CIVIL
STATE OF CALIFORNIA

THE STATE OF CALIFORNIA OR ITS OFFICERS OR AGENTS
SHALL NOT BE RESPONSIBLE FOR THE ACCURACY OR
COMPLETENESS OF SCANNED COPIES OF THIS PLAN SHEET.

THE REGISTERED CIVIL ENGINEER FOR THE PROJECT IS RESPONSIBLE FOR THE SELECTION
AND PROPER APPLICATION OF THE COMPONENT DESIGN AND ANY MODIFICATIONS SHOWN.

NOTE:
1. For locations of "SECTION A-A", "SECTION B-B" and details not shown, see "SOUND WALL MASONRY BLOCK ON RETAINING WALL DETAILS No. 1" sheet.

LEGEND:
CMU - Concrete Masonry Unit

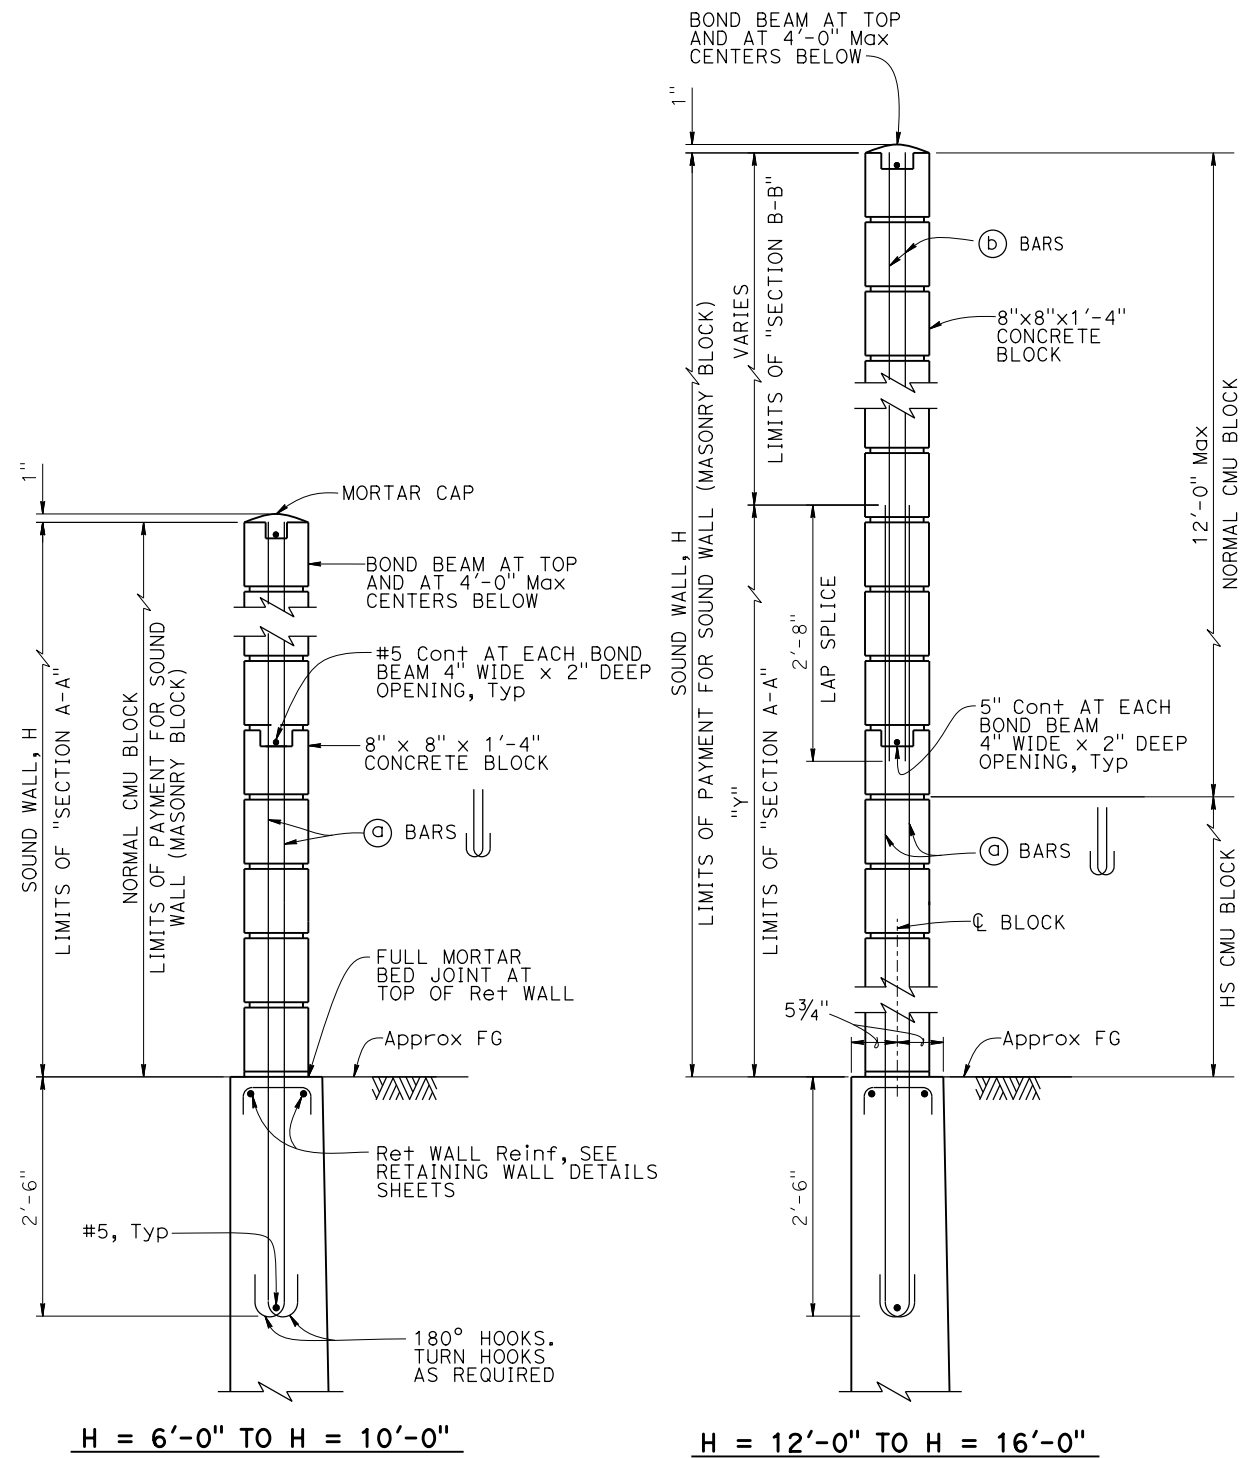


H = 6'-0" TO H = 10'-0"


H = 12'-0" TO H = 16'-0"

NOTE: For details not shown, see "H = 6'-0" TO H = 10'-0".

TYPICAL SECTION

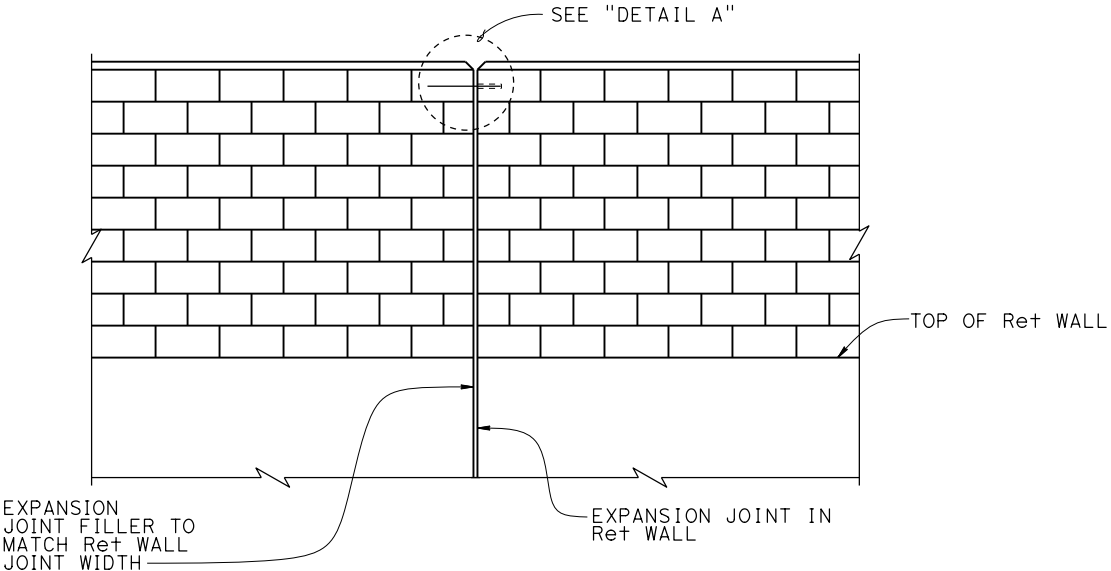

ALIGNMENT KEY DETAIL

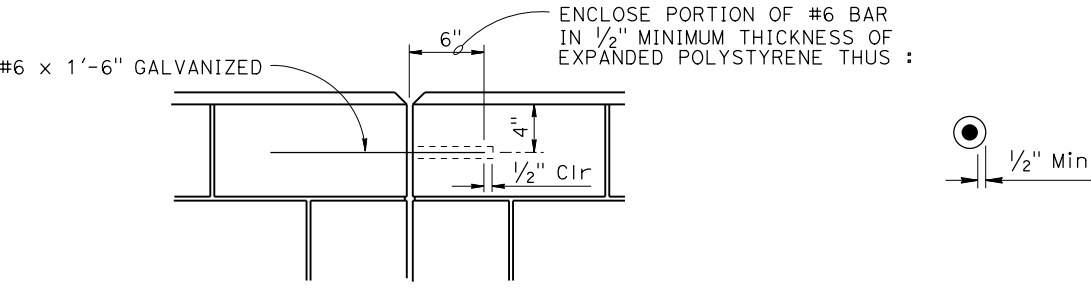

DETAIL A

NO SCALE