


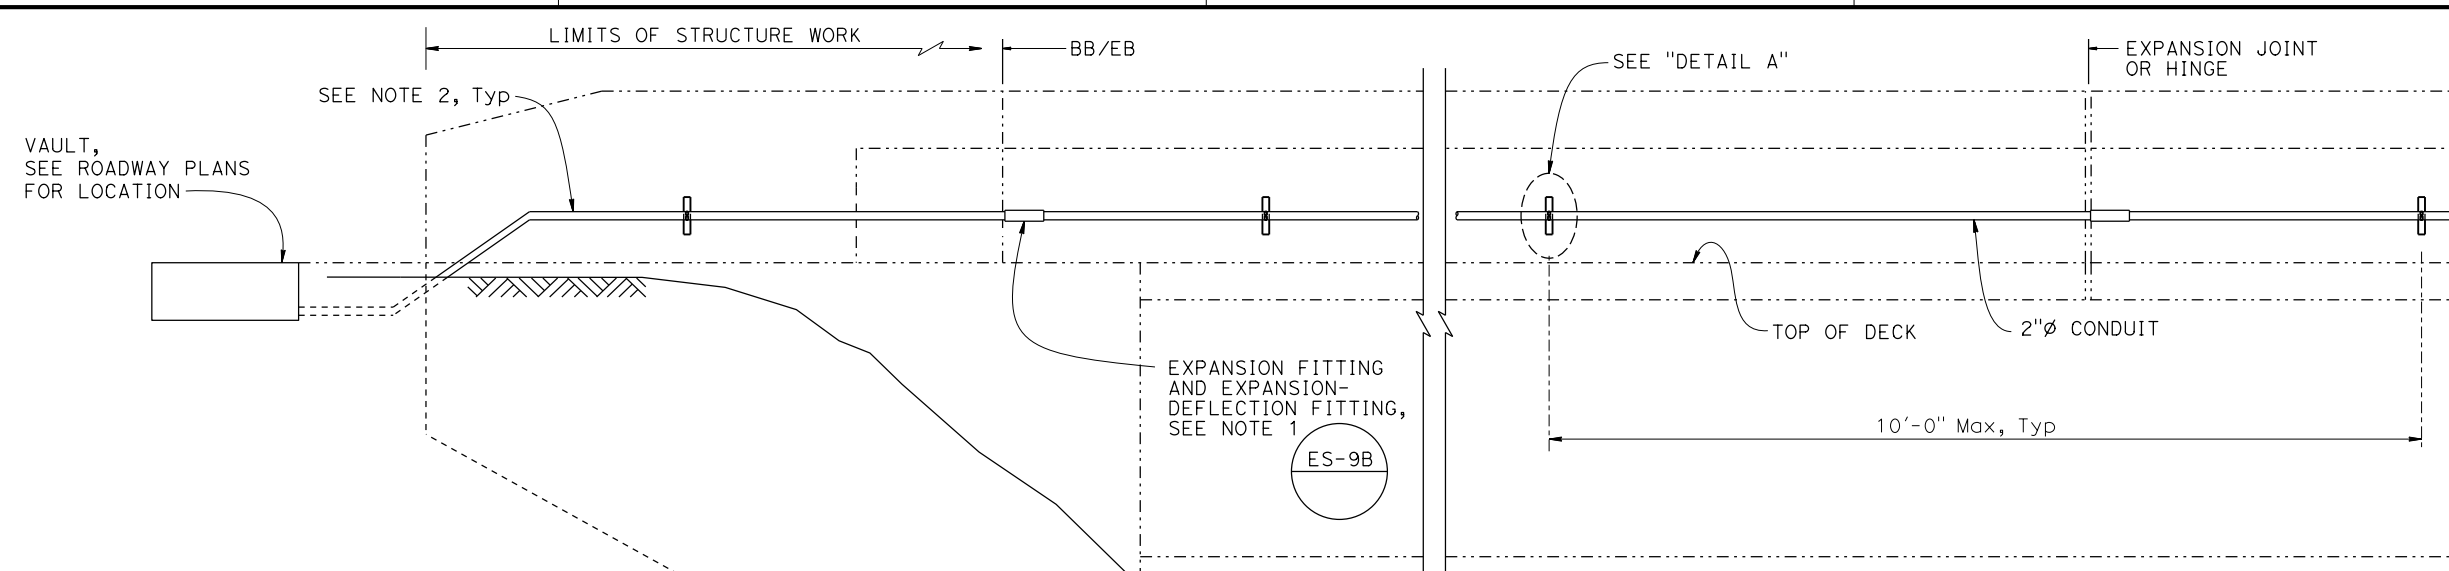

Dist	COUNTY	ROUTE	POST MILES TOTAL PROJECT	SHEET NO.	TOTAL SHEETS

REGISTERED CIVIL ENGINEER

DATE

PLANS APPROVAL DATE

THE STATE OF CALIFORNIA OR ITS OFFICERS OR AGENTS SHALL NOT BE RESPONSIBLE FOR THE ACCURACY OR COMPLETENESS OF SCANNED COPIES OF THIS PLAN SHEET.

THE REGISTERED CIVIL ENGINEER FOR THE PROJECT IS RESPONSIBLE FOR THE SELECTION AND PROPER APPLICATION OF THE COMPONENT DESIGN AND ANY MODIFICATIONS SHOWN.

REGISTERED PROFESSIONAL ENGINEER


No. X

Exp. X

CIVIL

STATE OF CALIFORNIA


- LEGEND:
----- Existing structure
MEA - Mechanical Expansion Anchor
- NOTES:
- Expansion fittings and expansion-deflection fittings shall be installed adjacent to BB, EB, joints or hinges (within 8 feet). Fittings must be able to handle up to the Movement Range (MR) noted for the bridge. For expansion fitting installation, see "EXPANSION FITTING INSTALLATION POSITION TABLE."
 - For vault locations and other details not shown, see ROADWAY PLANS.
 - For additional details and "OPTIONAL COVER DETAIL", see "COMMUNICATION CONDUIT (ATTACHMENT DETAILS)" sheet.
 - For 2"Ø conduits, a minimum bend radius of 1'-8" is required if the total bend degrees between pull point/vaults is 90 degrees or less. For total bend degrees from 90 to 180, the minimum bend radius for all bend fittings is 2'-0".
 - All mounting hardware shall be protected against corrosion.

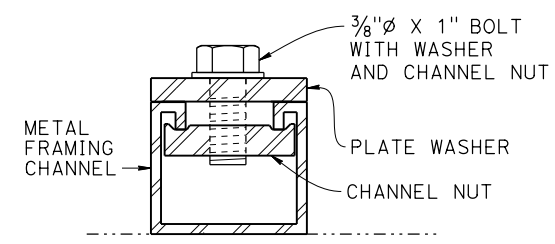

SECTION C-C
NO SCALE

PART ELEVATION
NO SCALE

NOTE: Concrete Barrier (Type 736) shown, other barriers similar.

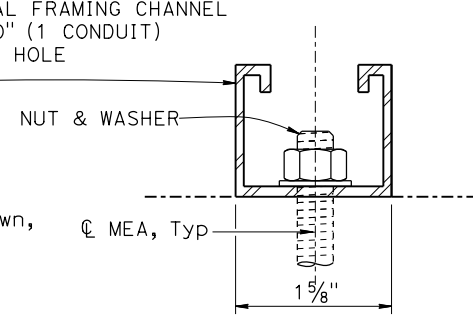

SECTION B-B
NO SCALE


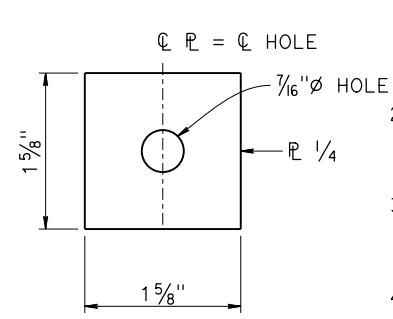



PLATE WASHER
NO SCALE

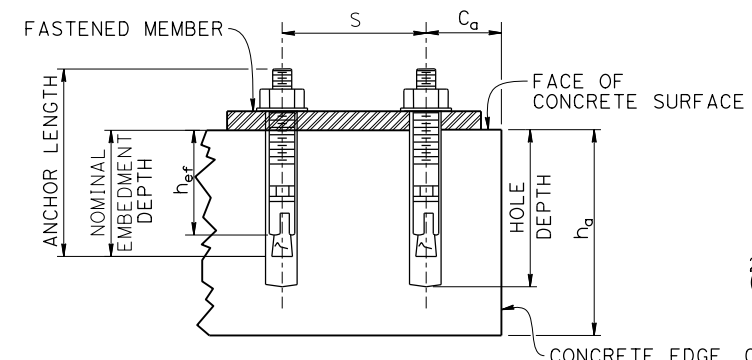


TYPICAL STUD TYPE (WEDGE) STUD MEA

EXPANSION FITTING INSTALLATION POSITION TABLE	
INSTALLATION PERIOD	% OF MAXIMUM EXPANSION RANGE
December to February	80%
March to May and September to November	50%
June to August	20%


CONCRETE ANCHORAGE REQUIREMENTS				
Anchor Diameter (in)	Minimum Effective Embedment h _{ef} (in)	Minimum Concrete Thickness h _a (in)	Minimum Edge Distance c _a (in)	Minimum Anchor Spacing S (in)
3/8	1 1/2	6	6	3

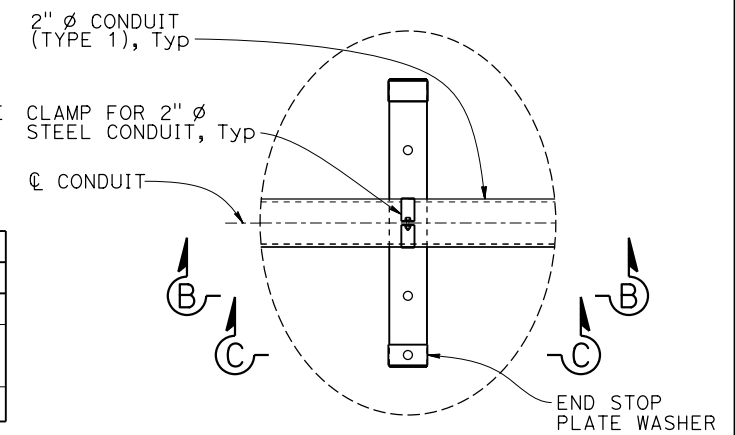

DETAIL A
NO SCALE

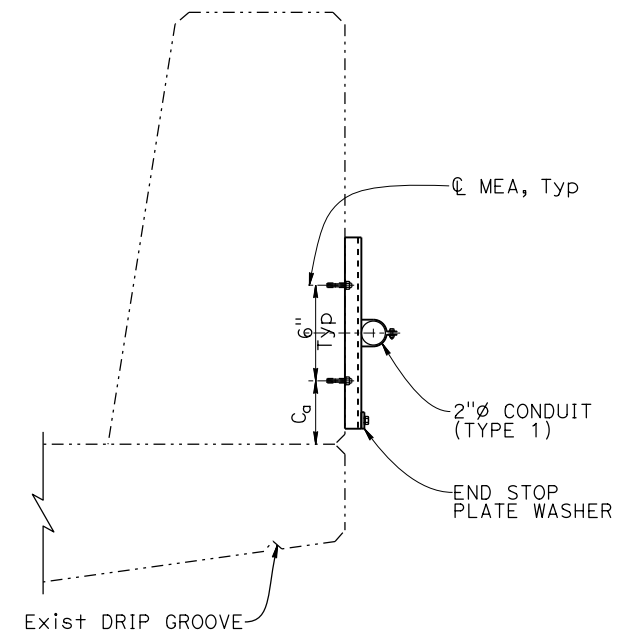

BARRIER (NO INSET)

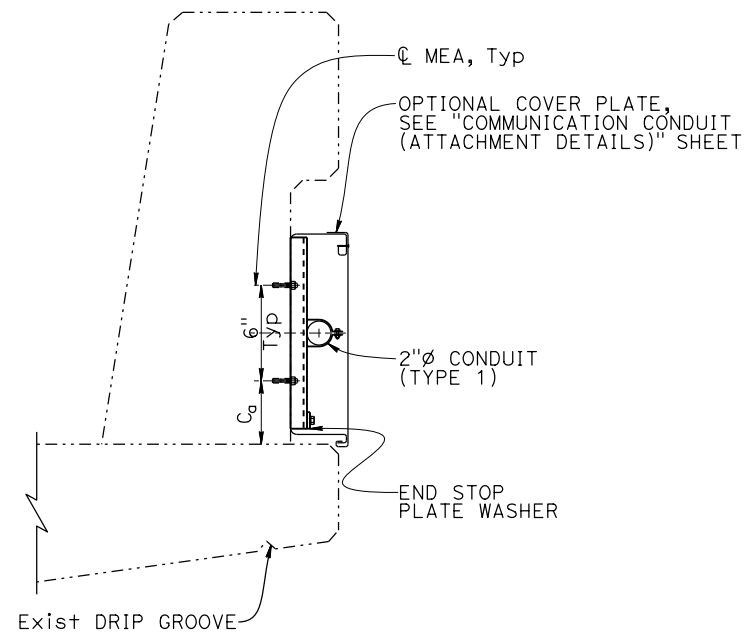

BARRIER (INSET)

ATTACHMENT DETAIL
NO SCALE