


- NOTES:
- Adjust spacing of #4 hoops at post location as necessary to avoid locations of the threaded rods attaching the tubular handrailing to the top of the upper beam, see "TUBULAR HANDRAILING DETAIL" on the "CONCRETE BARRIER TYPE 86HSW DETAILS No. 5" sheet.
 - For reinforcement at approach end block, see "CONCRETE BARRIER TYPE 86HSW DETAILS No. 6" sheet. Reinforcement at departure end block is similar to approach end block except as shown in "SECTION E-E", shown on "CONCRETE BARRIER TYPE 86HSW DETAILS No. 2" sheet.
 - For details not shown, see "CONCRETE BARRIER TYPE 86HSW DETAILS No. 1" sheet and "CONCRETE BARRIER TYPE 86HSW DETAILS No. 2" sheet.

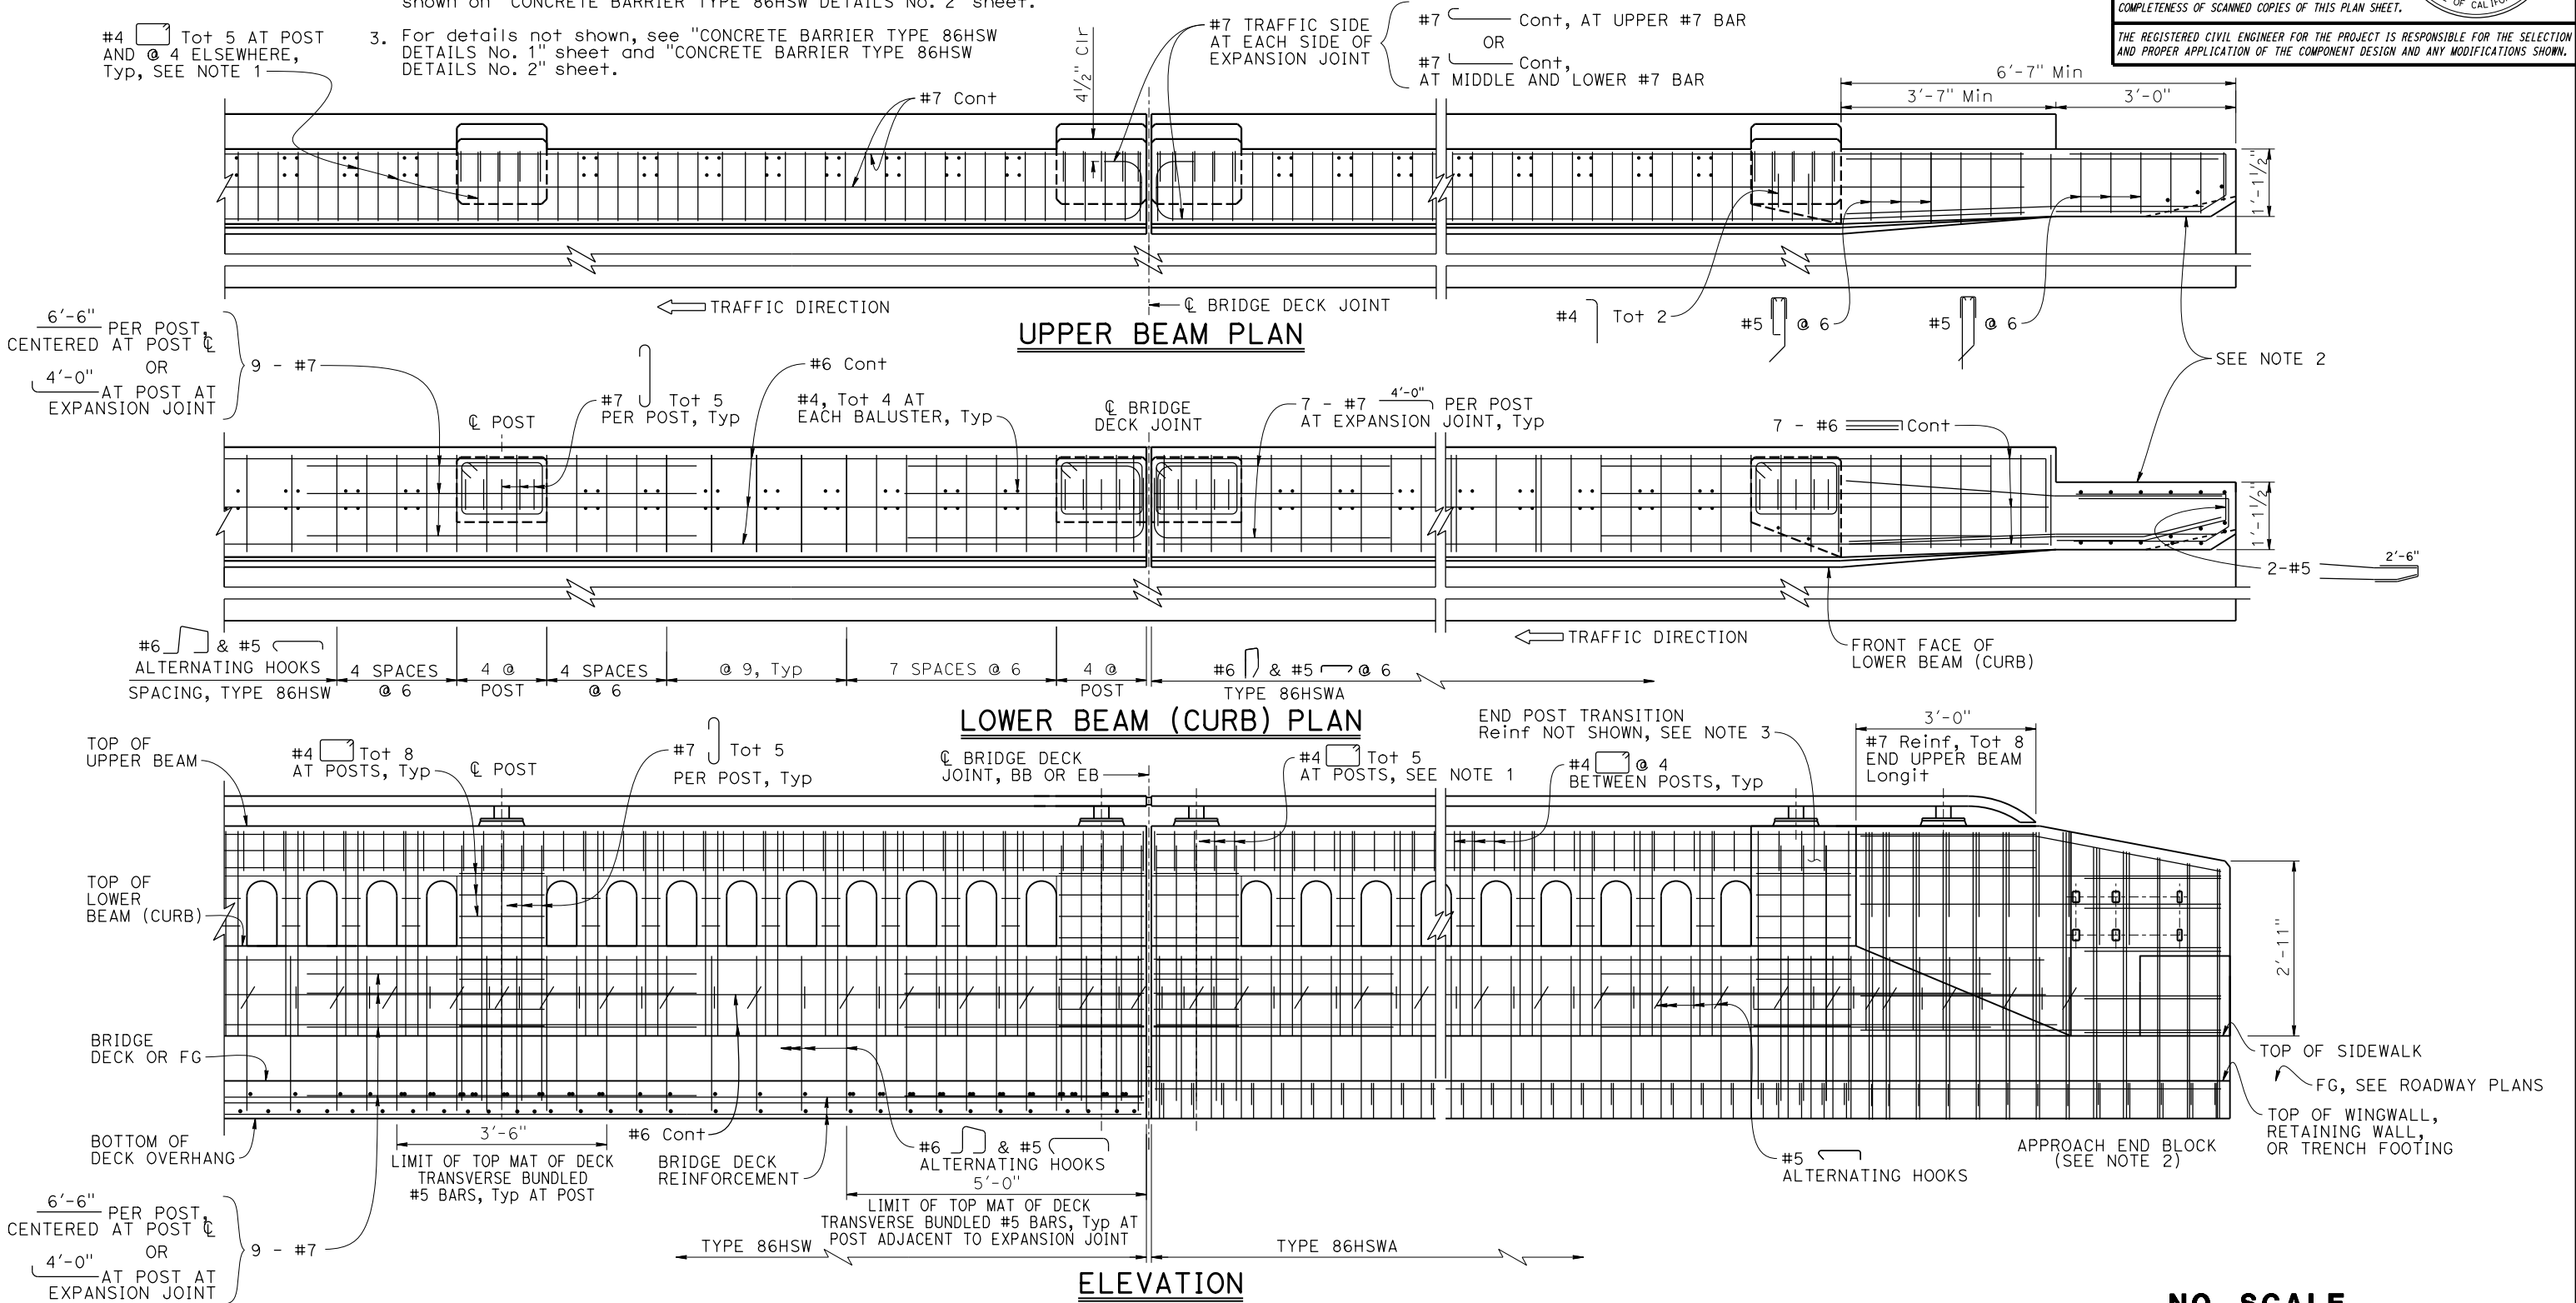

DIST	COUNTY	ROUTE	POST MILES TOTAL PROJECT	SHEET NO.	TOTAL SHEETS

REGISTERED CIVIL ENGINEER X DATE

PLANS APPROVAL DATE

THE STATE OF CALIFORNIA OR ITS OFFICERS OR AGENTS SHALL NOT BE RESPONSIBLE FOR THE ACCURACY OR COMPLETENESS OF SCANNED COPIES OF THIS PLAN SHEET.

THE REGISTERED CIVIL ENGINEER FOR THE PROJECT IS RESPONSIBLE FOR THE SELECTION AND PROPER APPLICATION OF THE COMPONENT DESIGN AND ANY MODIFICATIONS SHOWN.