



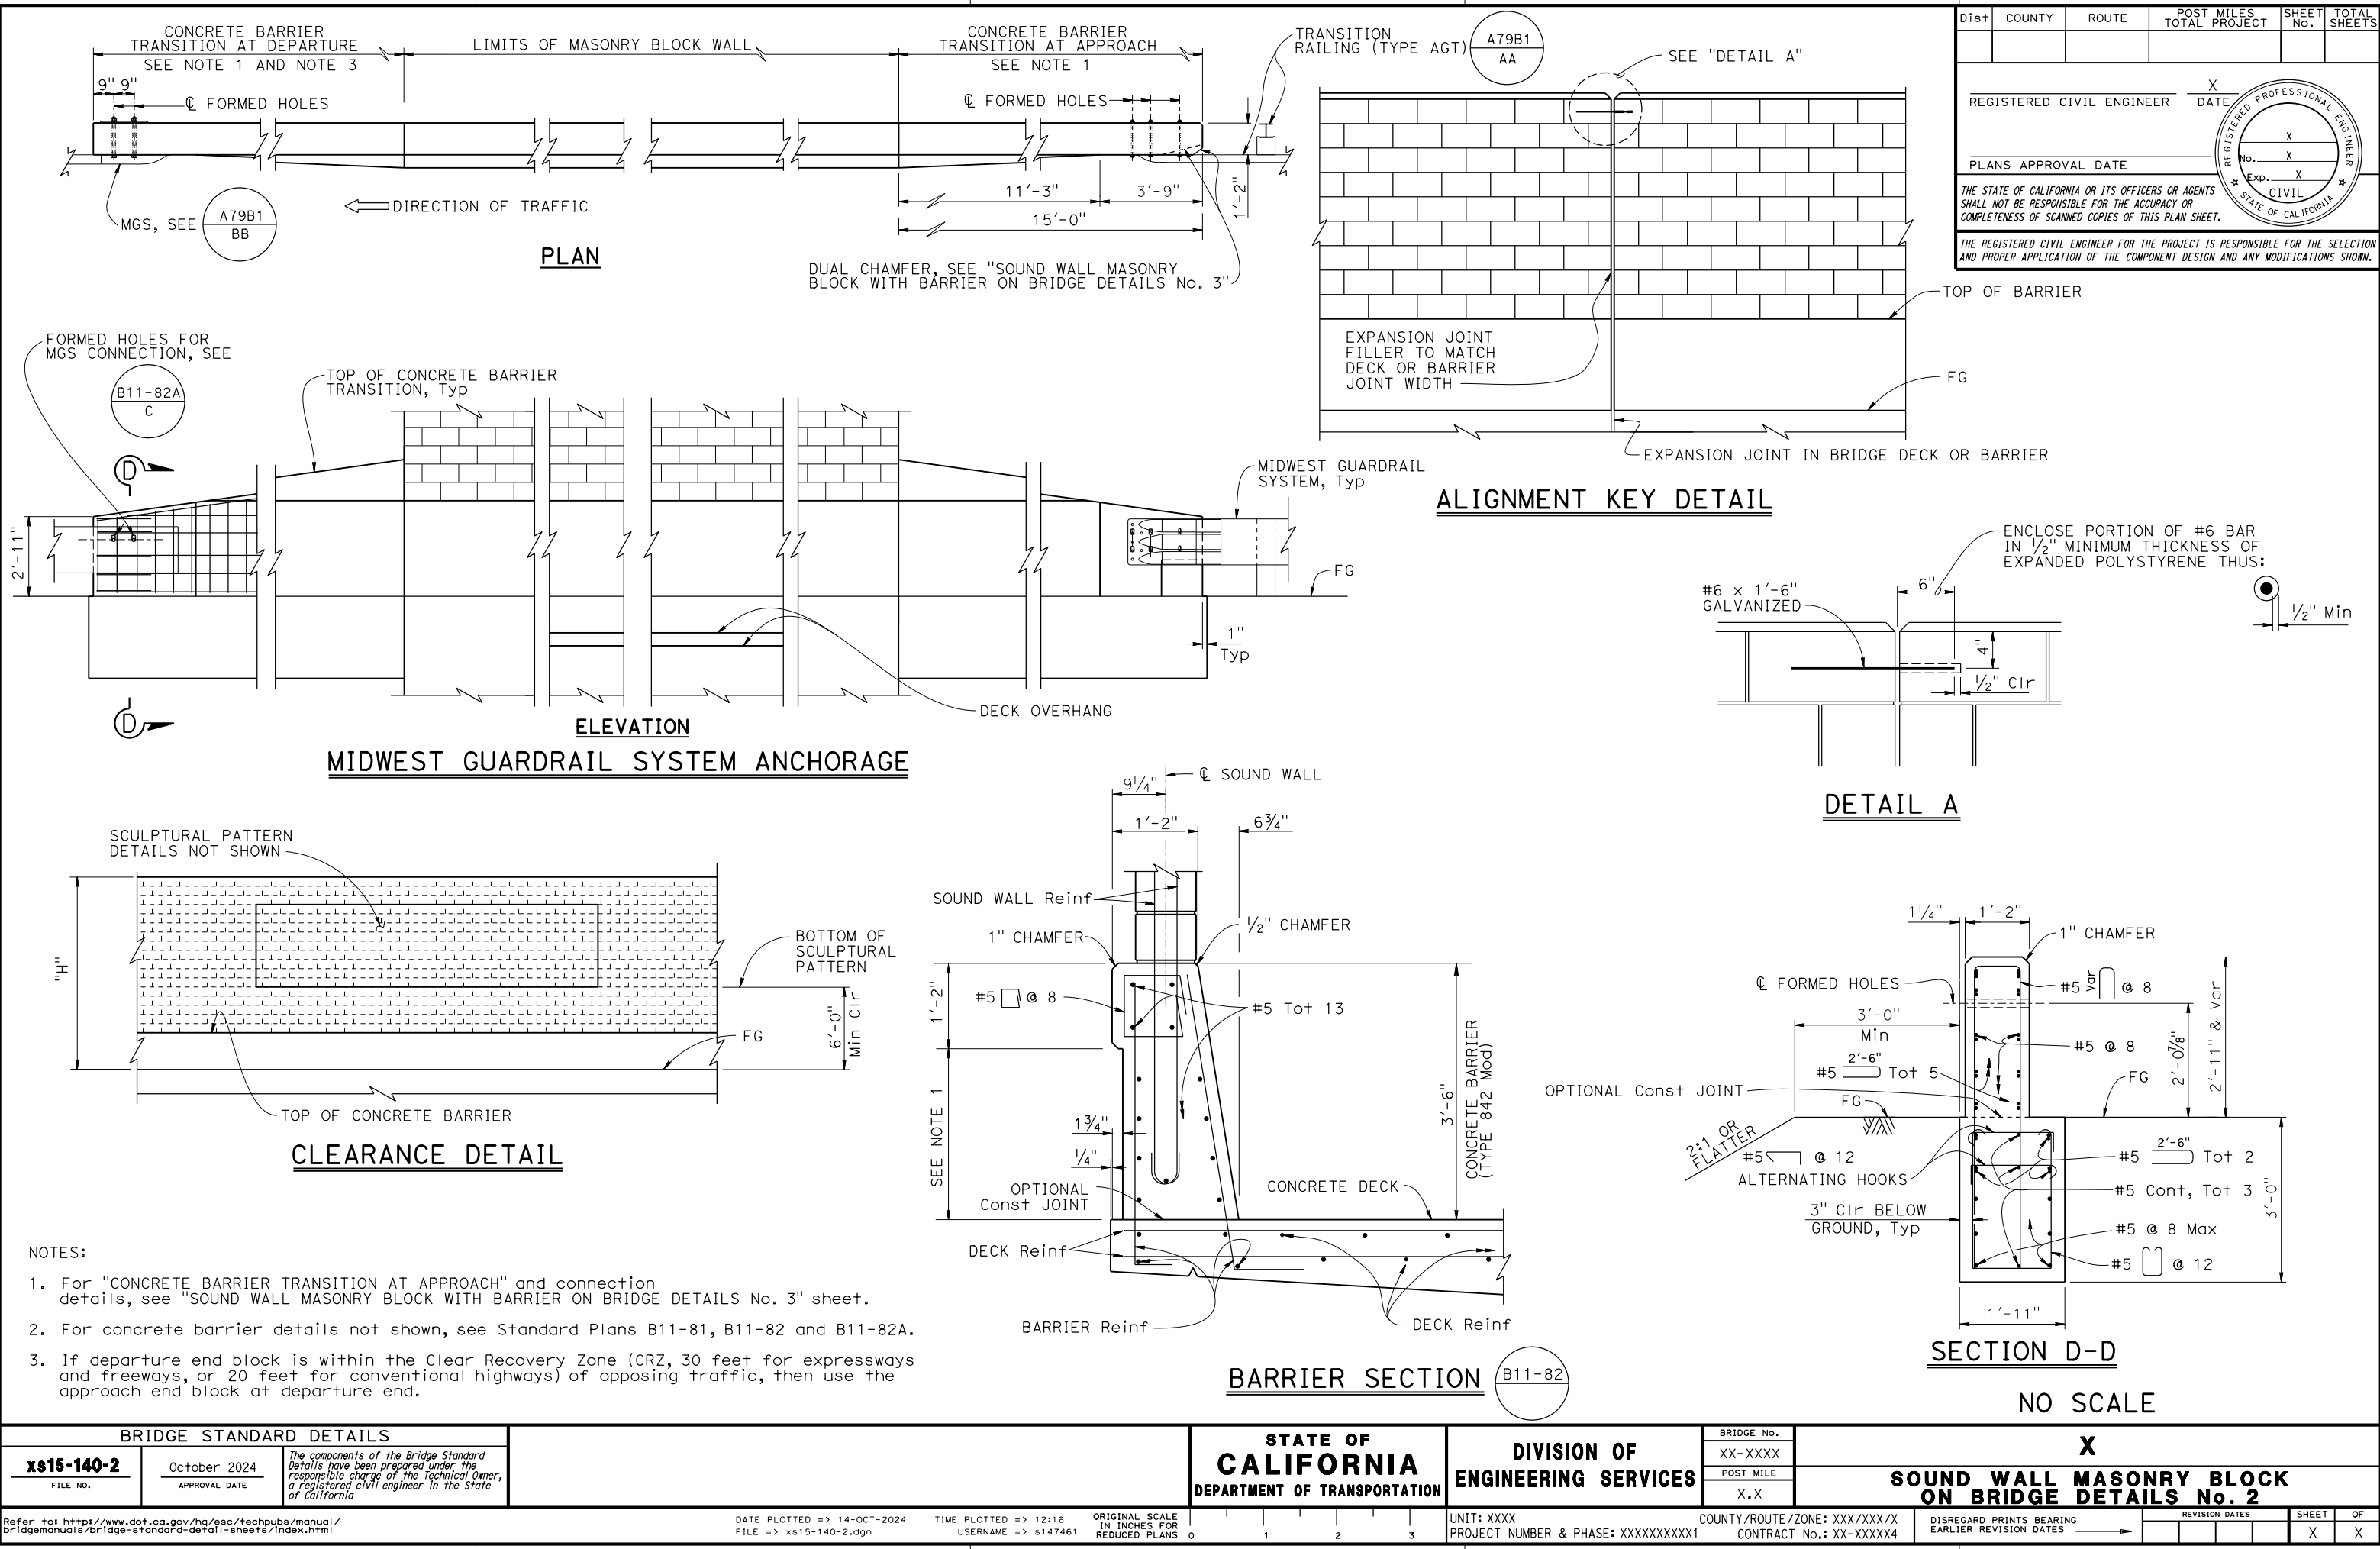

Dist	COUNTY	ROUTE	POST MILES TOTAL PROJECT	SHEET No.	TOTAL SHEETS
REGISTERED CIVIL ENGINEER			X	DATE	
PLANS APPROVAL DATE					
THE STATE OF CALIFORNIA OR ITS OFFICERS OR AGENTS SHALL NOT BE RESPONSIBLE FOR THE ACCURACY OR COMPLETENESS OF SCANNED COPIES OF THIS PLAN SHEET.					
THE REGISTERED CIVIL ENGINEER FOR THE PROJECT IS RESPONSIBLE FOR THE SELECTION AND PROPER APPLICATION OF THE COMPONENT DESIGN AND ANY MODIFICATIONS SHOWN.					

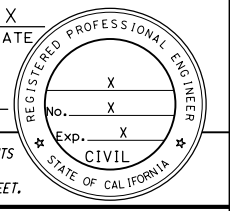

- NOTES:
- For "CONCRETE BARRIER TRANSITION AT APPROACH" and connection details, see "SOUND WALL MASONRY BLOCK WITH BARRIER ON BRIDGE DETAILS No. 3" sheet.
 - For concrete barrier details not shown, see Standard Plans B11-81, B11-82 and B11-82A.
 - If departure end block is within the Clear Recovery Zone (CRZ, 30 feet for expressways and freeways, or 20 feet for conventional highways) of opposing traffic, then use the approach end block at departure end.

BRIDGE STANDARD DETAILS			STATE OF CALIFORNIA		DIVISION OF ENGINEERING SERVICES		X		SOUND WALL MASONRY BLOCK ON BRIDGE DETAILS No. 2	
x815-140-2	October 2024	The components of the Bridge Standard Details have been prepared under the responsible charge of the Technical Owner, a registered civil engineer in the State of California	DEPARTMENT OF TRANSPORTATION		BRIDGE No. XX-XXXX		POST MILE X.X		COUNTY/ROUTE/ZONE: XXX/XXX/X	
FILE NO.	APPROVAL DATE								CONTRACT No.: XX-XXXXX4	
Refer to: http://www.dot.ca.gov/hq/esc/techpubs/manual/bridgemanuals/bridge-standard-detail-sheets/index.html			DATE PLOTTED => 14-OCT-2024		TIME PLOTTED => 12:16		ORIGINAL SCALE IN INCHES FOR REDUCED PLANS		UNIT: XXXX PROJECT NUMBER & PHASE: XXXXXXXXXX1	
FILE => x815-140-2.dgn			USERNAME => s147461						DISREGARD PRINTS BEARING EARLIER REVISION DATES	
									REVISION DATES	
									SHEET OF	
									X X	